


尺寸图

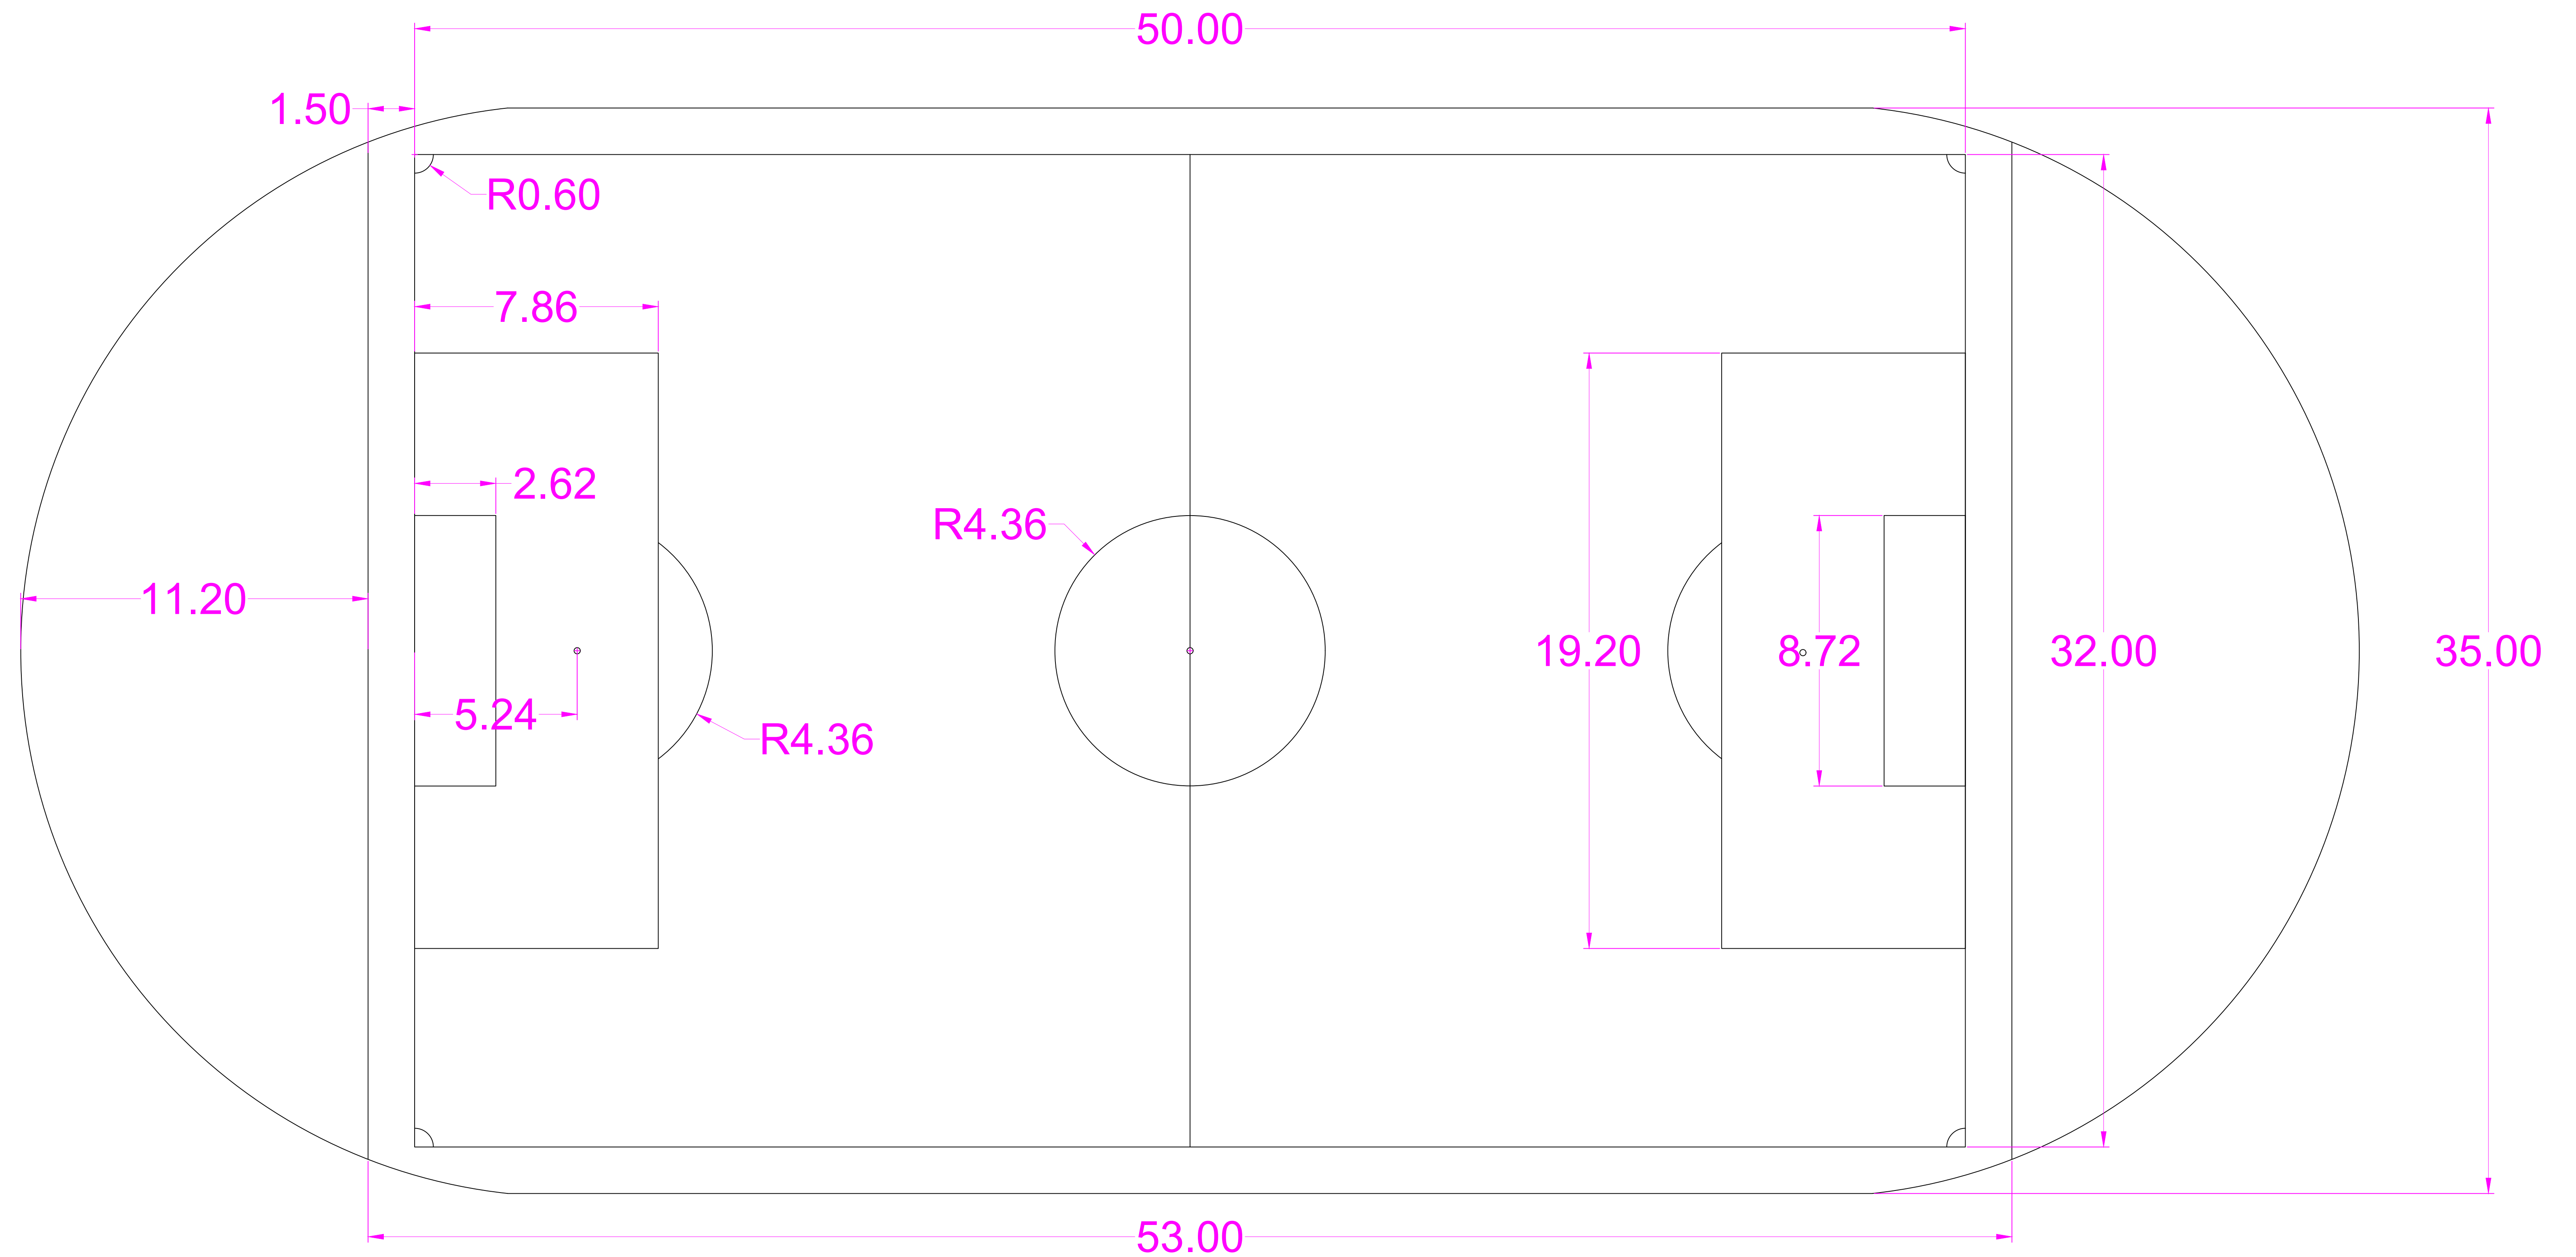


备注:

1. 场地比赛区域尺寸50.00m*32.00m，白草宽度0.08m；
2. 现场施工时，请按照设计图纸的草卷编号顺序摆放，否则因此造成的铺装问题公司概不承担责任；
3. 施工时请按照设计图纸的胶水用量以确保粘接效果。

工程名称	
图纸类型	七人制人造草坪效果施工图
制图单位	
日期	2026年6月1日


效果图

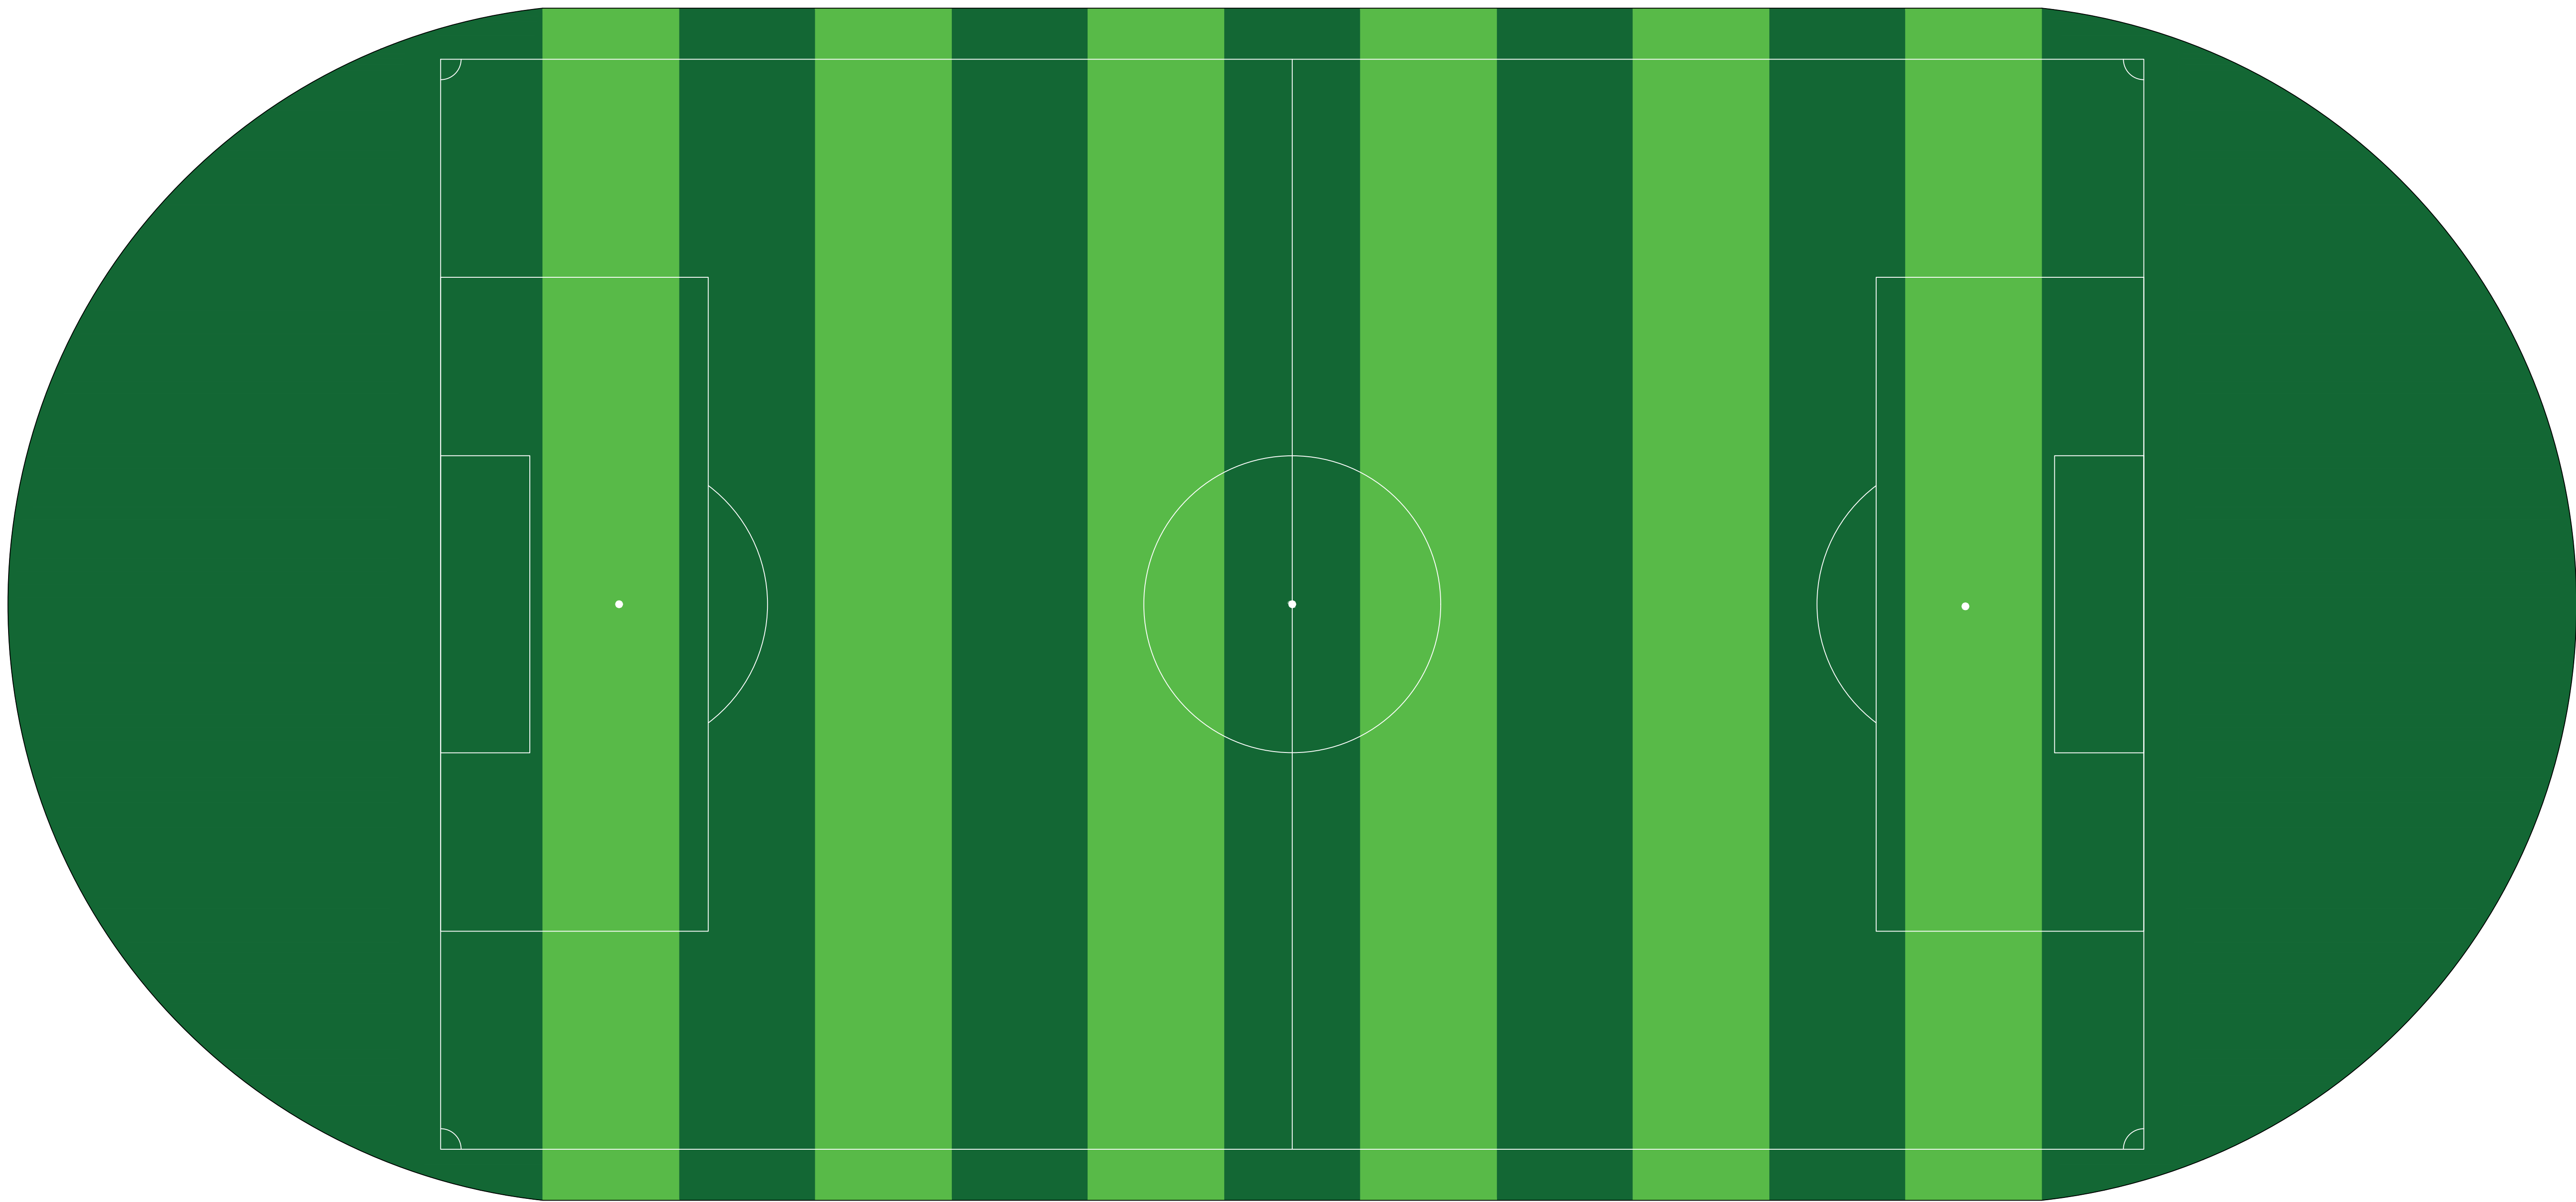

- 备注：
- 1. 场地比赛区域尺寸50.00m*32.00m，白草宽度0.08m；
 - 2. 现场施工时，请按照设计图纸的草卷编号顺序摆放，否则因此造成的铺装问题公司概不承担责任；
 - 3. 施工时请按照设计图纸的胶水用量以确保粘接效果。

工程名称	
图纸类型	七人制人造草坪效果施工图
制图单位	
日期	2026年6月1日

施工图

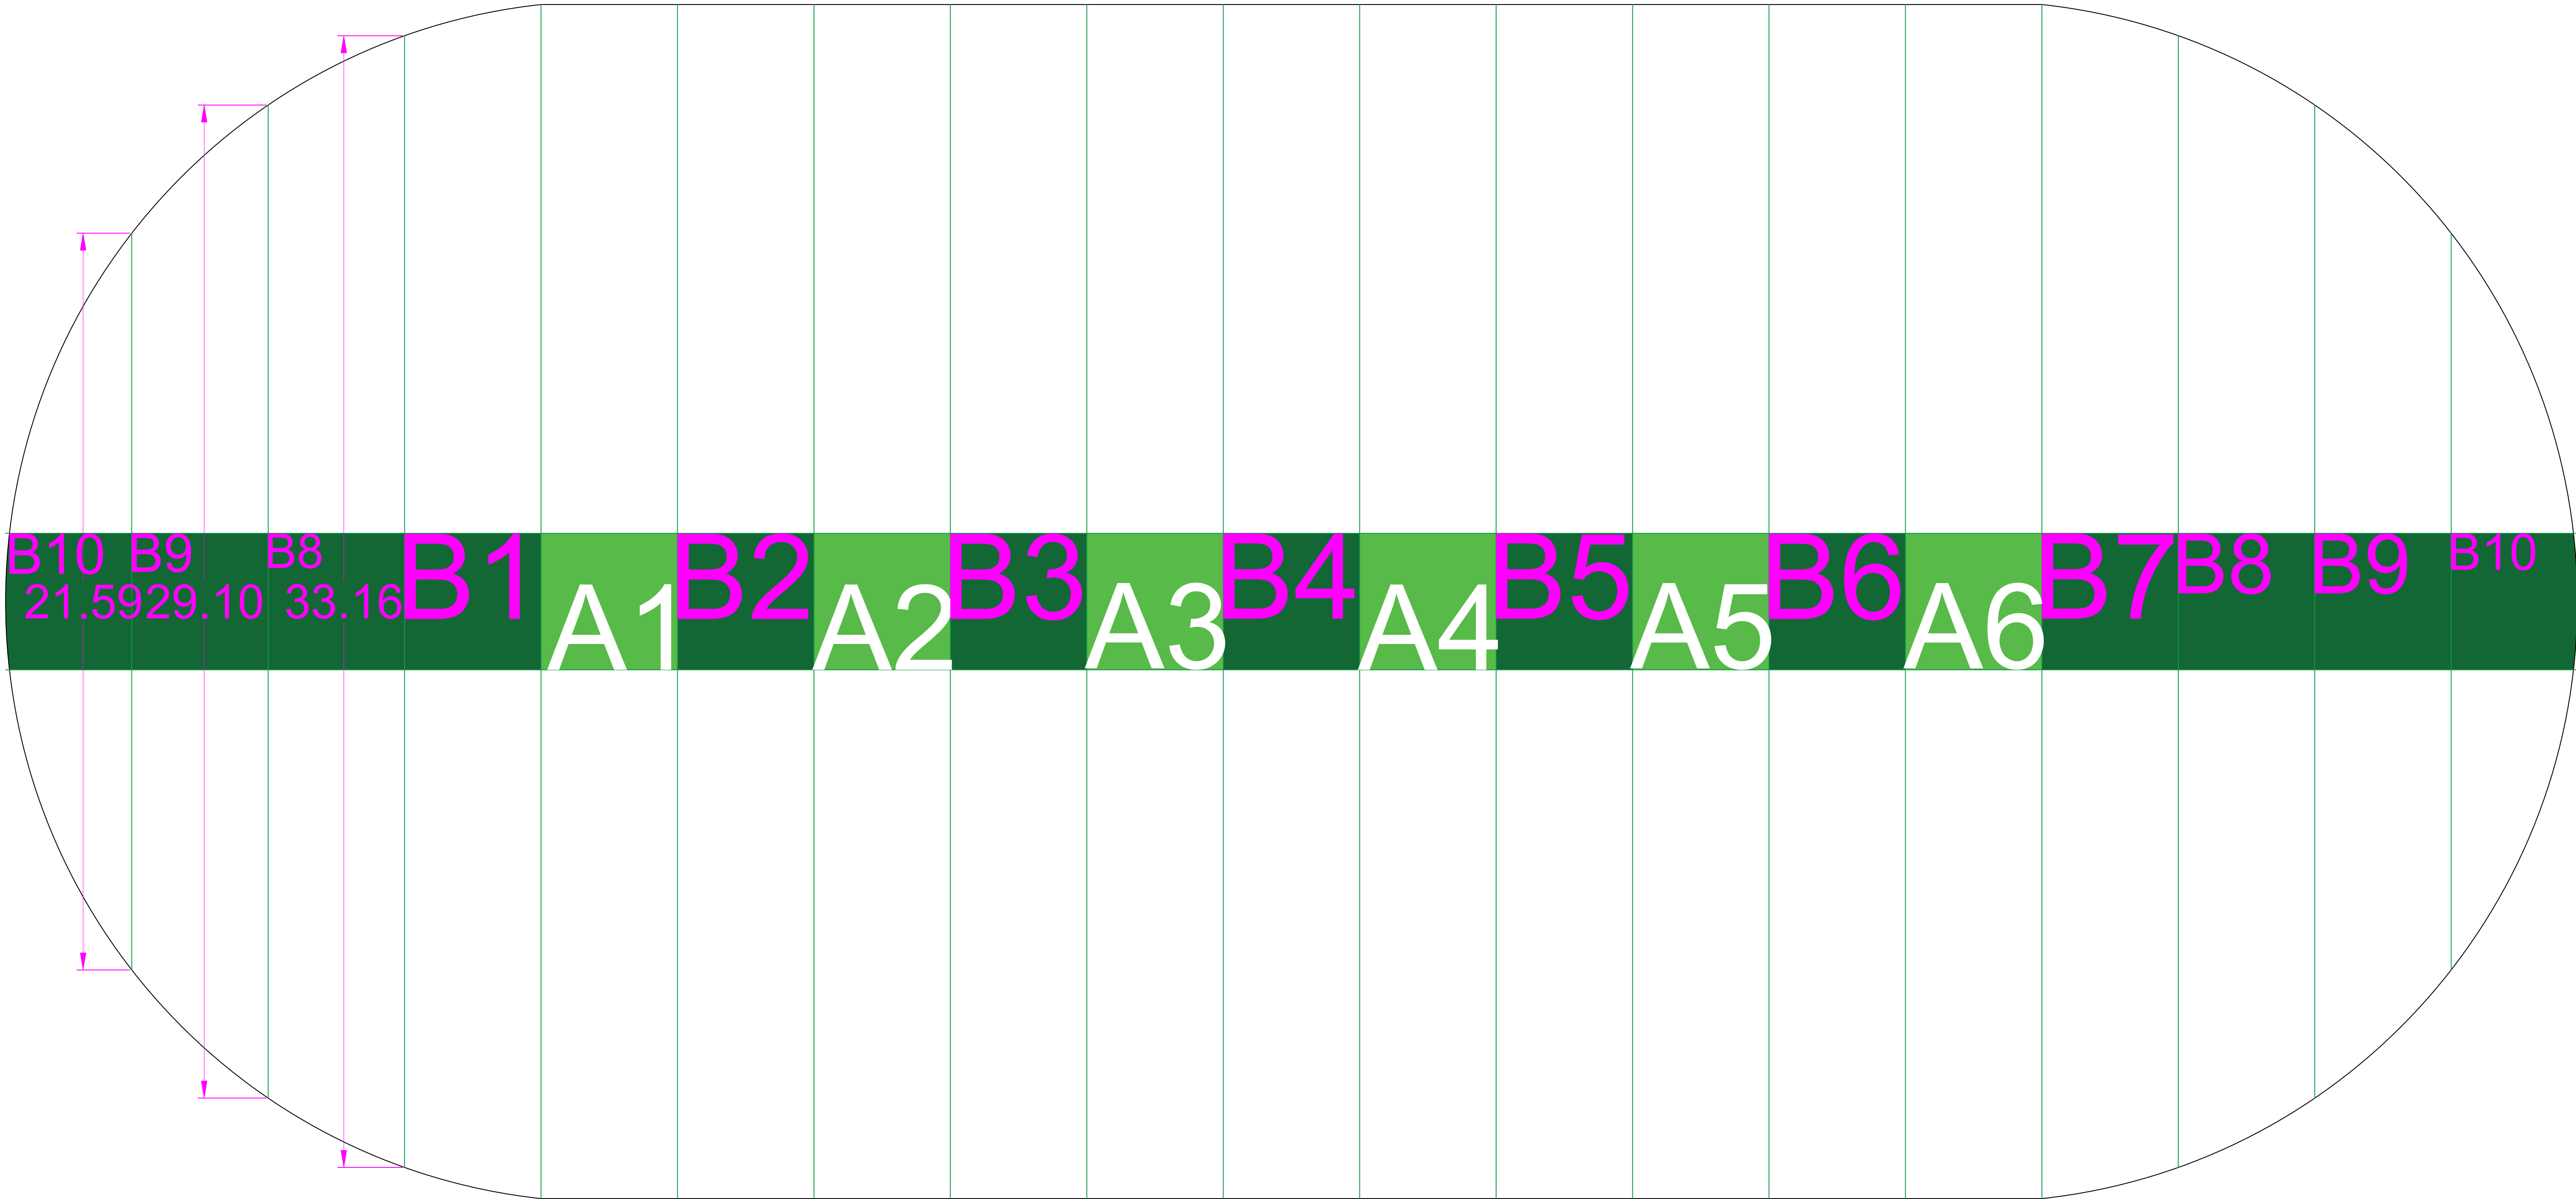

草坪生产方案明细表						
序号	颜色	规格	卷数	单位	数量	编号
1	浅色	35*4m	6	m²	840	A1-A6
2	深色	35*4m	7	m²	980	B1-B7
3	深色B8	33.16*4m	2	m²	265.28	B8
4	深色B9	29.1*4m	2	m²	232.8	B9
5	深色B10	21.59*4m	2	m²	172.72	B10
6	白草	16*2m	1	m²	32	AW1
7	胶水			桶		
8	接缝布			米		
9	场地实际面积：2380.5m² 实际生产面积：2522.80m²（绿草2490.8, 白草32m²）					

工程名称	
图纸类型	七人制人造草坪效果施工图
制图单位	
日期	2026年6月1日