


尺寸图

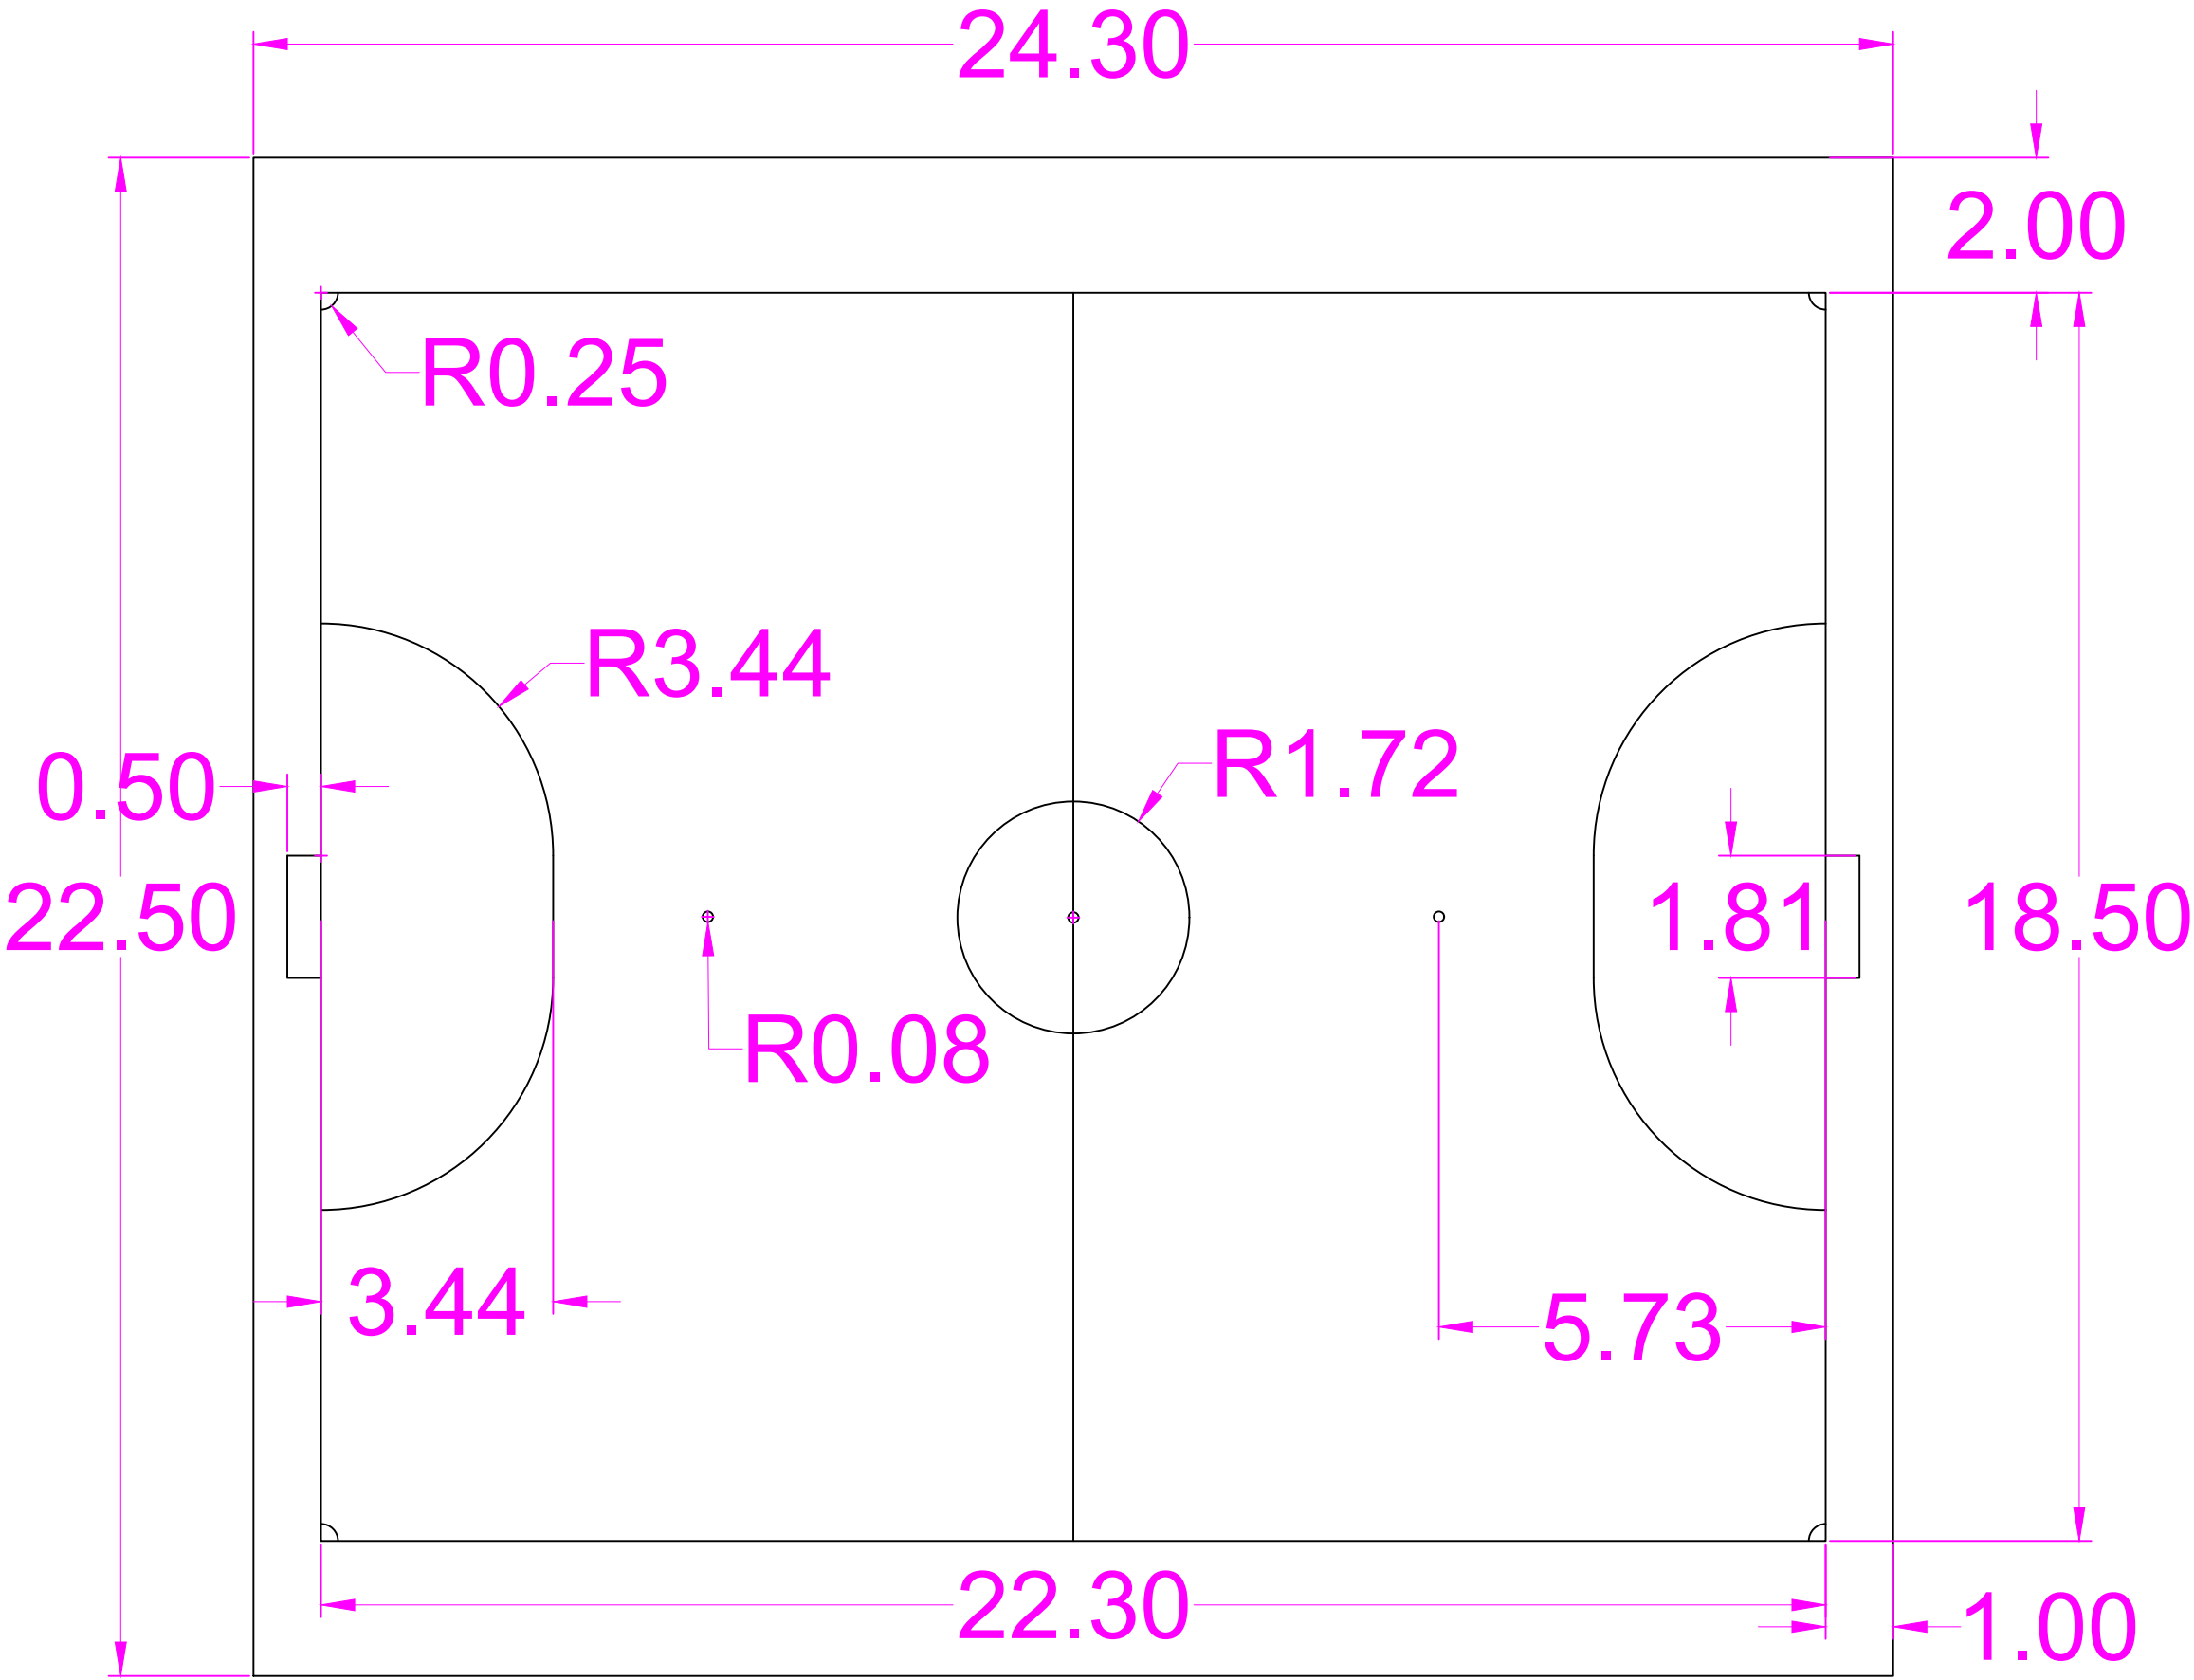

备注:


- 1. 场地比赛区域尺寸22.30m*18.50m，白草宽度0.08m；
- 2. 现场施工时，请按照设计图纸的草卷编号顺序摆放，否则因此造成的铺装问题公司概不承担责任；
- 3. 施工时请按照设计图纸的胶水用量以确保粘接效果。

工程名称	
图纸类型	五人制人造草坪施工图
制图单位	
日期	2026年01月14日

效果图

2.15

2.15

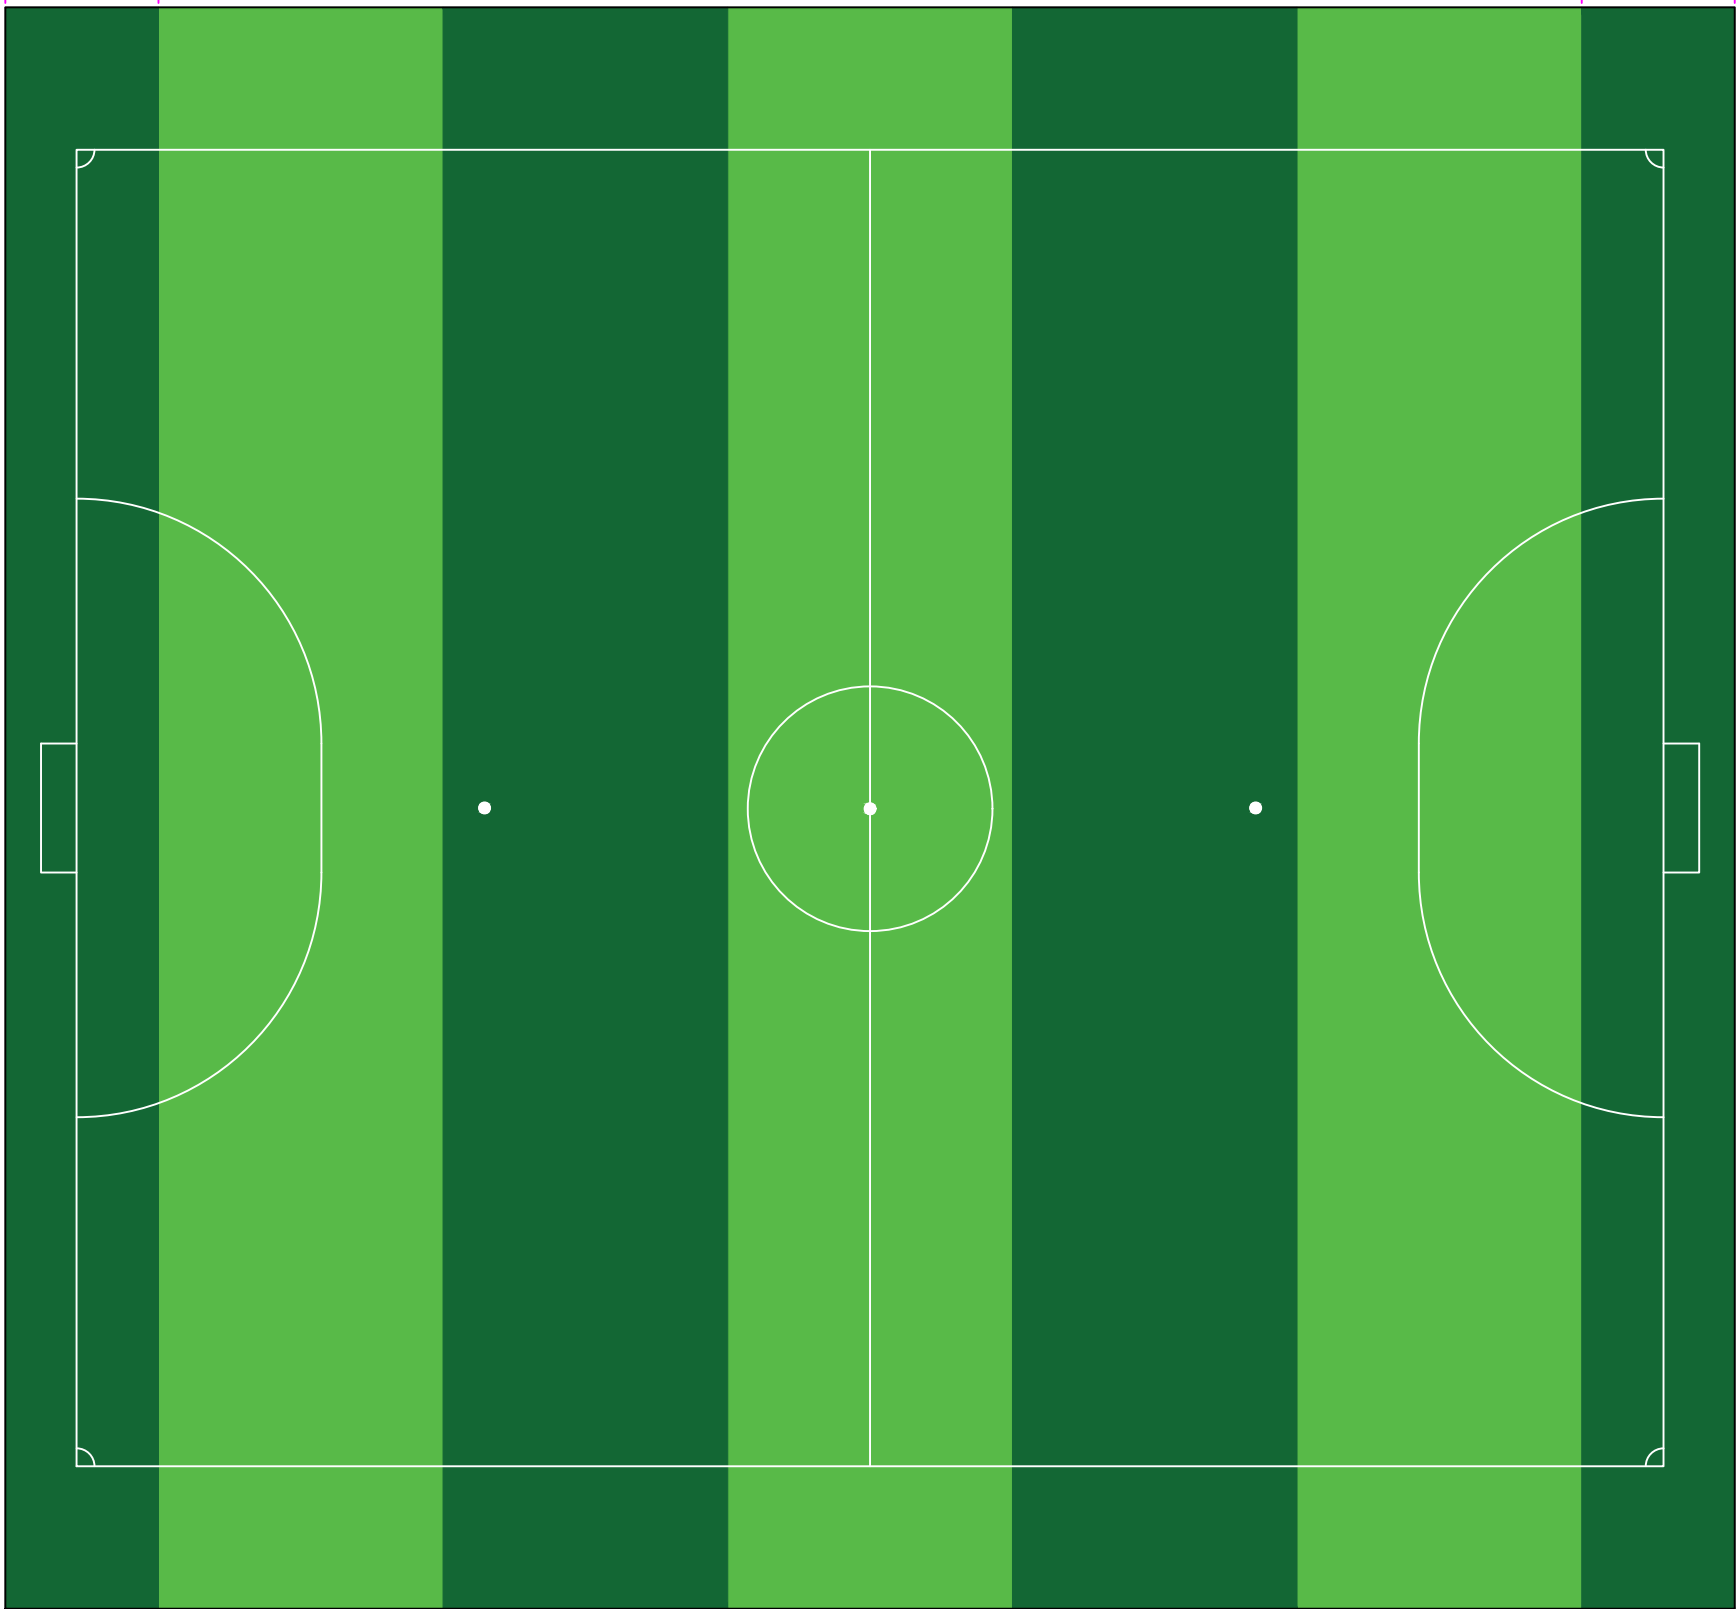


备注：

- 1. 场地比赛区域尺寸22.30m*18.50m，白草宽度0.08m；
- 2. 现场施工时，请按照设计图纸的草卷编号顺序摆放，否则因此造成的铺装问题公司概不承担责任；
- 3. 施工时请按照设计图纸的胶水用量以确保粘接效果。

工程名称	
图纸类型	五人制人造草坪施工图
制图单位	
日期	2026年01月14日

施工图

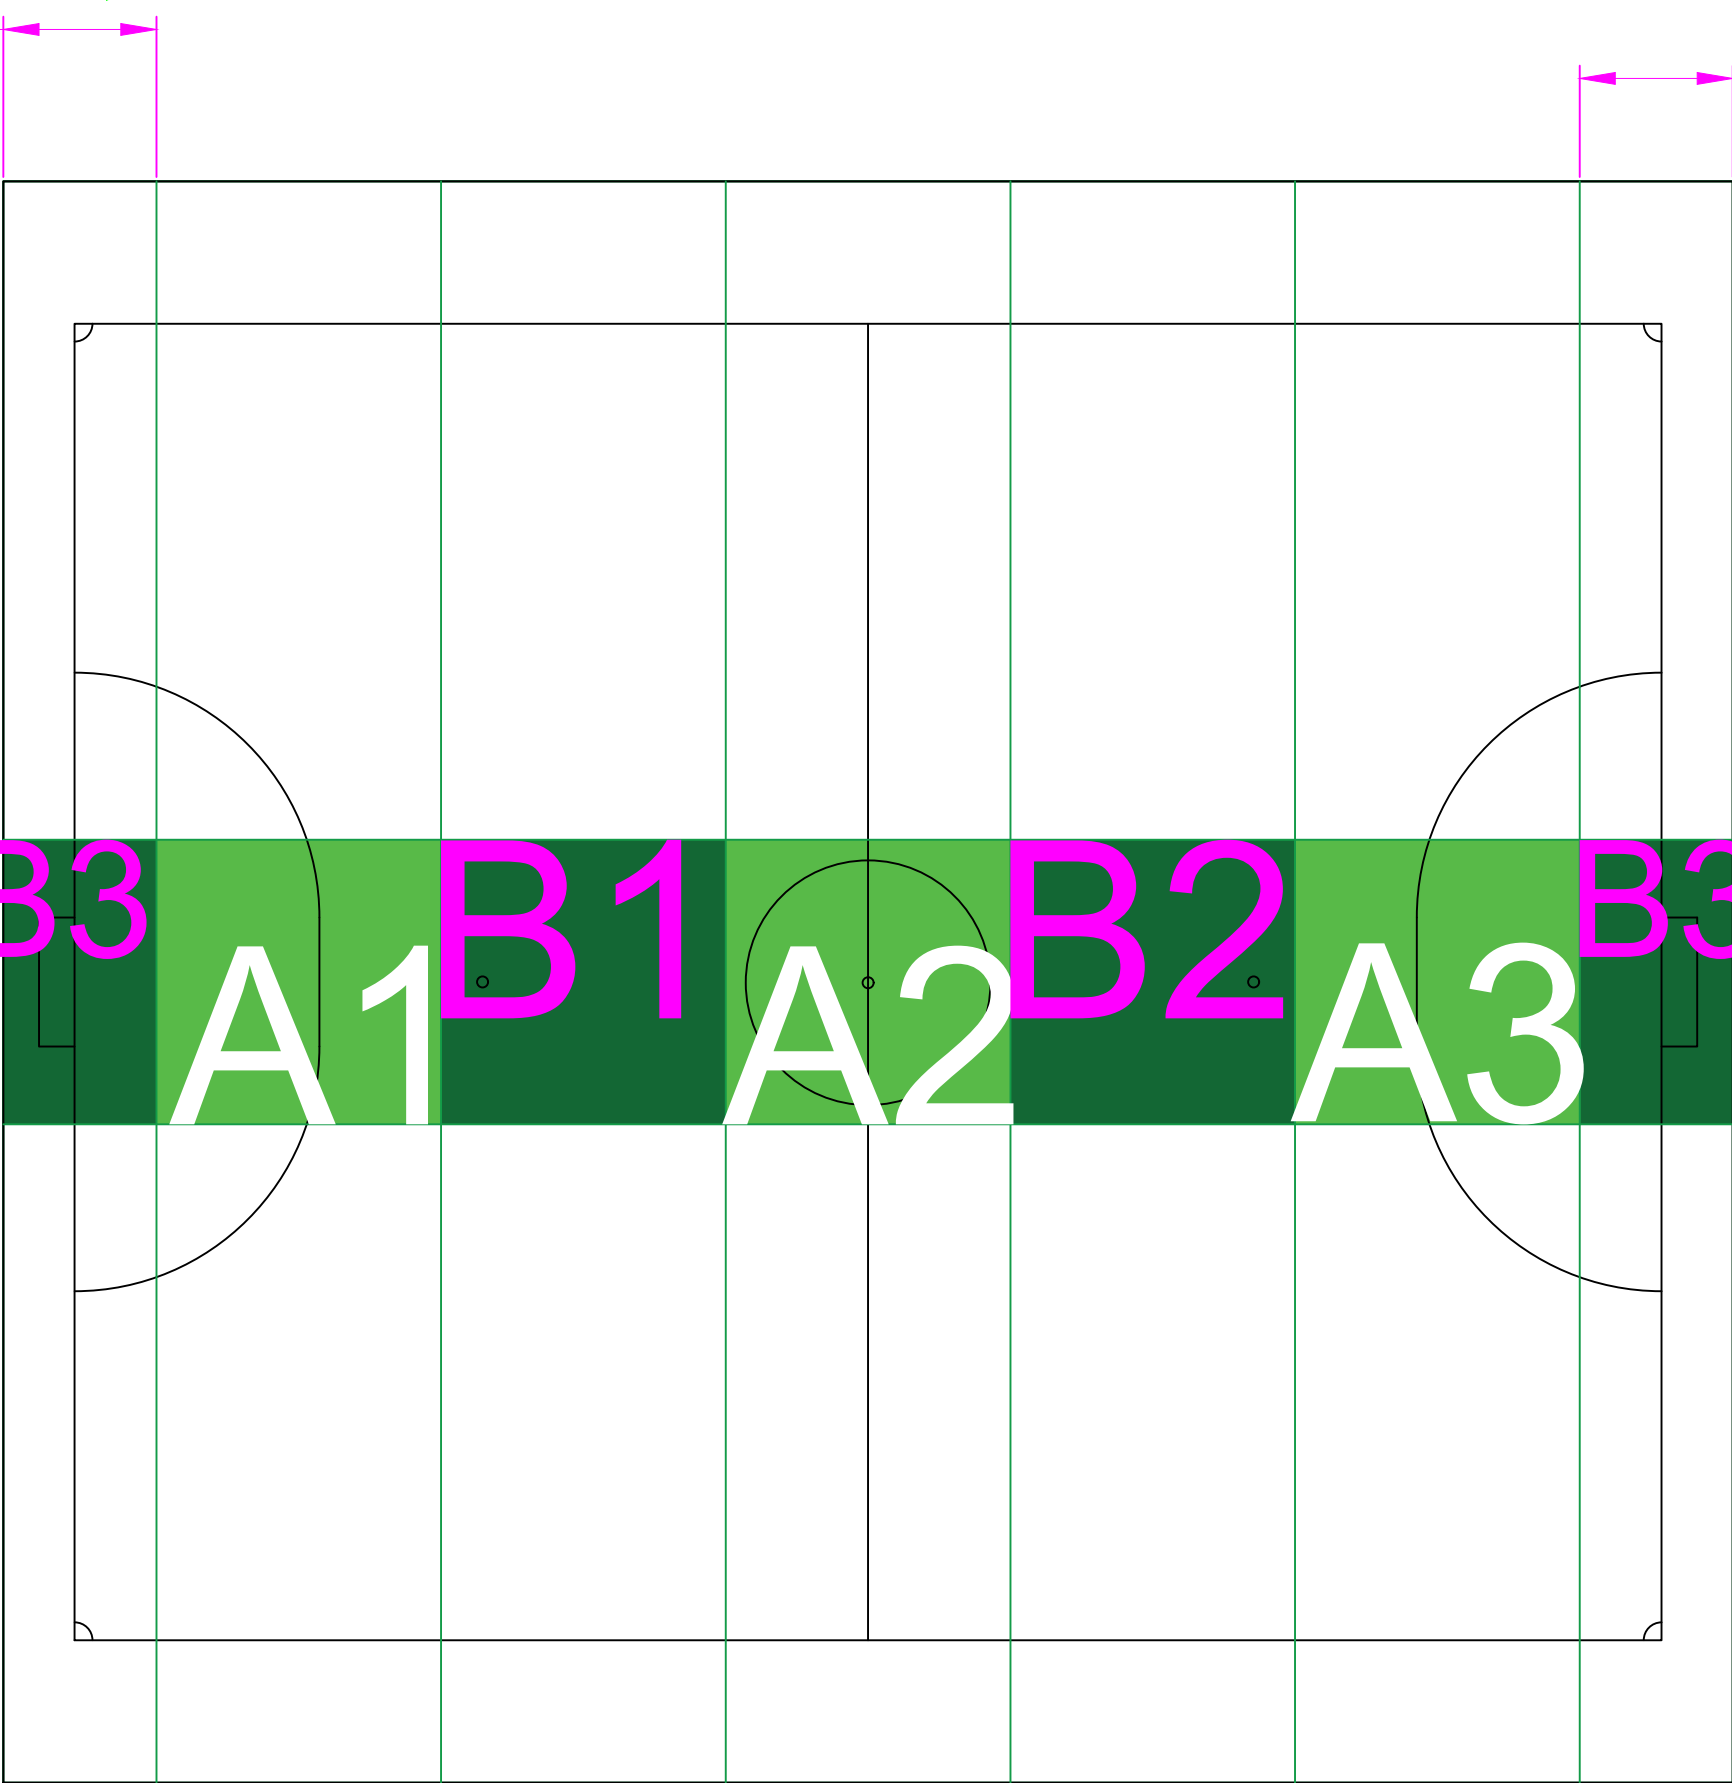

草坪生产方案明细表						
序号	颜色	规格	卷数	单位	数量	编号
1	浅色	22. 50*4m	3	m²	270.00	A1-A3
2	深色	22. 50*4m	2	m²	180.00	B1-B2
3	深色	24. 20*4m	1	m²	96.80	B3
4	白草	6*2m	1	m²	12.00	AW1
5	胶水		8	桶		
6	接缝布			米	900	
7	场地实际面积：546. 75m²		实际生产面积：558. 80m²（绿草546. 8m²，白草12m²）			

工程名称	
图纸类型	五人制人造草坪施工图
制图单位	
日期	2026年01月14日