


尺寸图

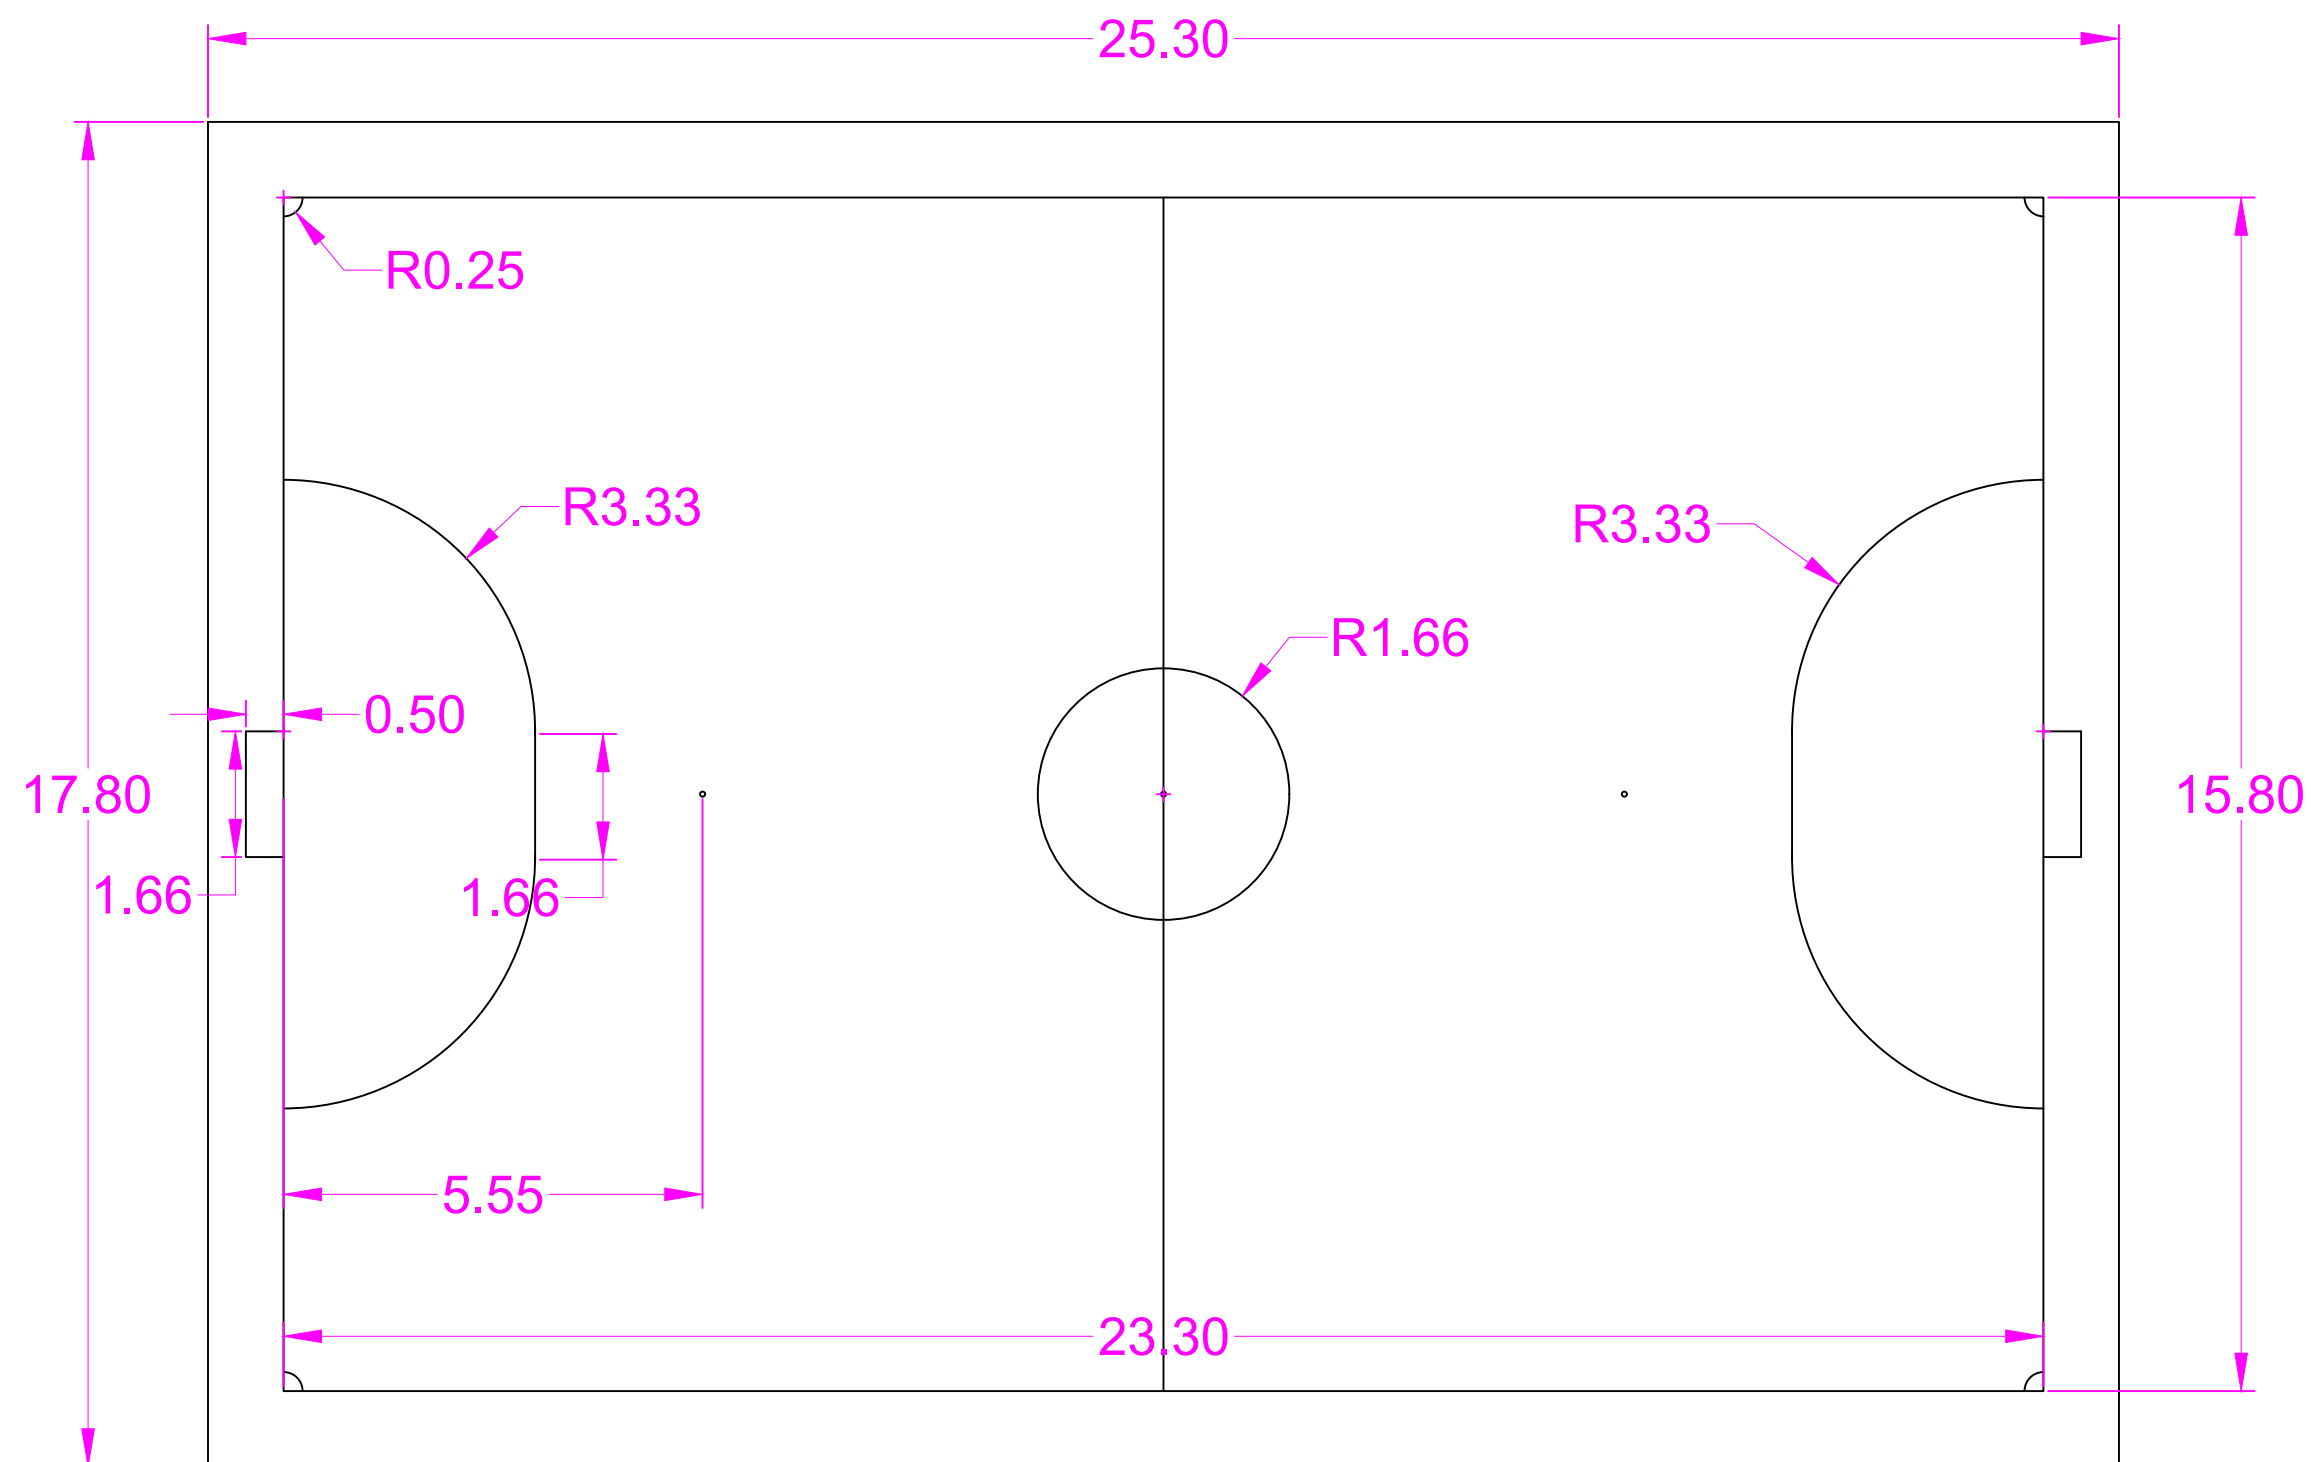


备注:

1. 场地比赛区域尺寸23.3m*15.80m，白草宽度0.08m；
2. 现场施工时，请按照设计图纸的草卷编号顺序摆放，否则因此造成的铺装问题公司概不承担责任；
3. 施工时请按照设计图纸的胶水用量以确保粘接效果。

工程名称	
图纸类型	五人制人造草坪施工图
制图单位	
日期	2026. 7. 30

效果图

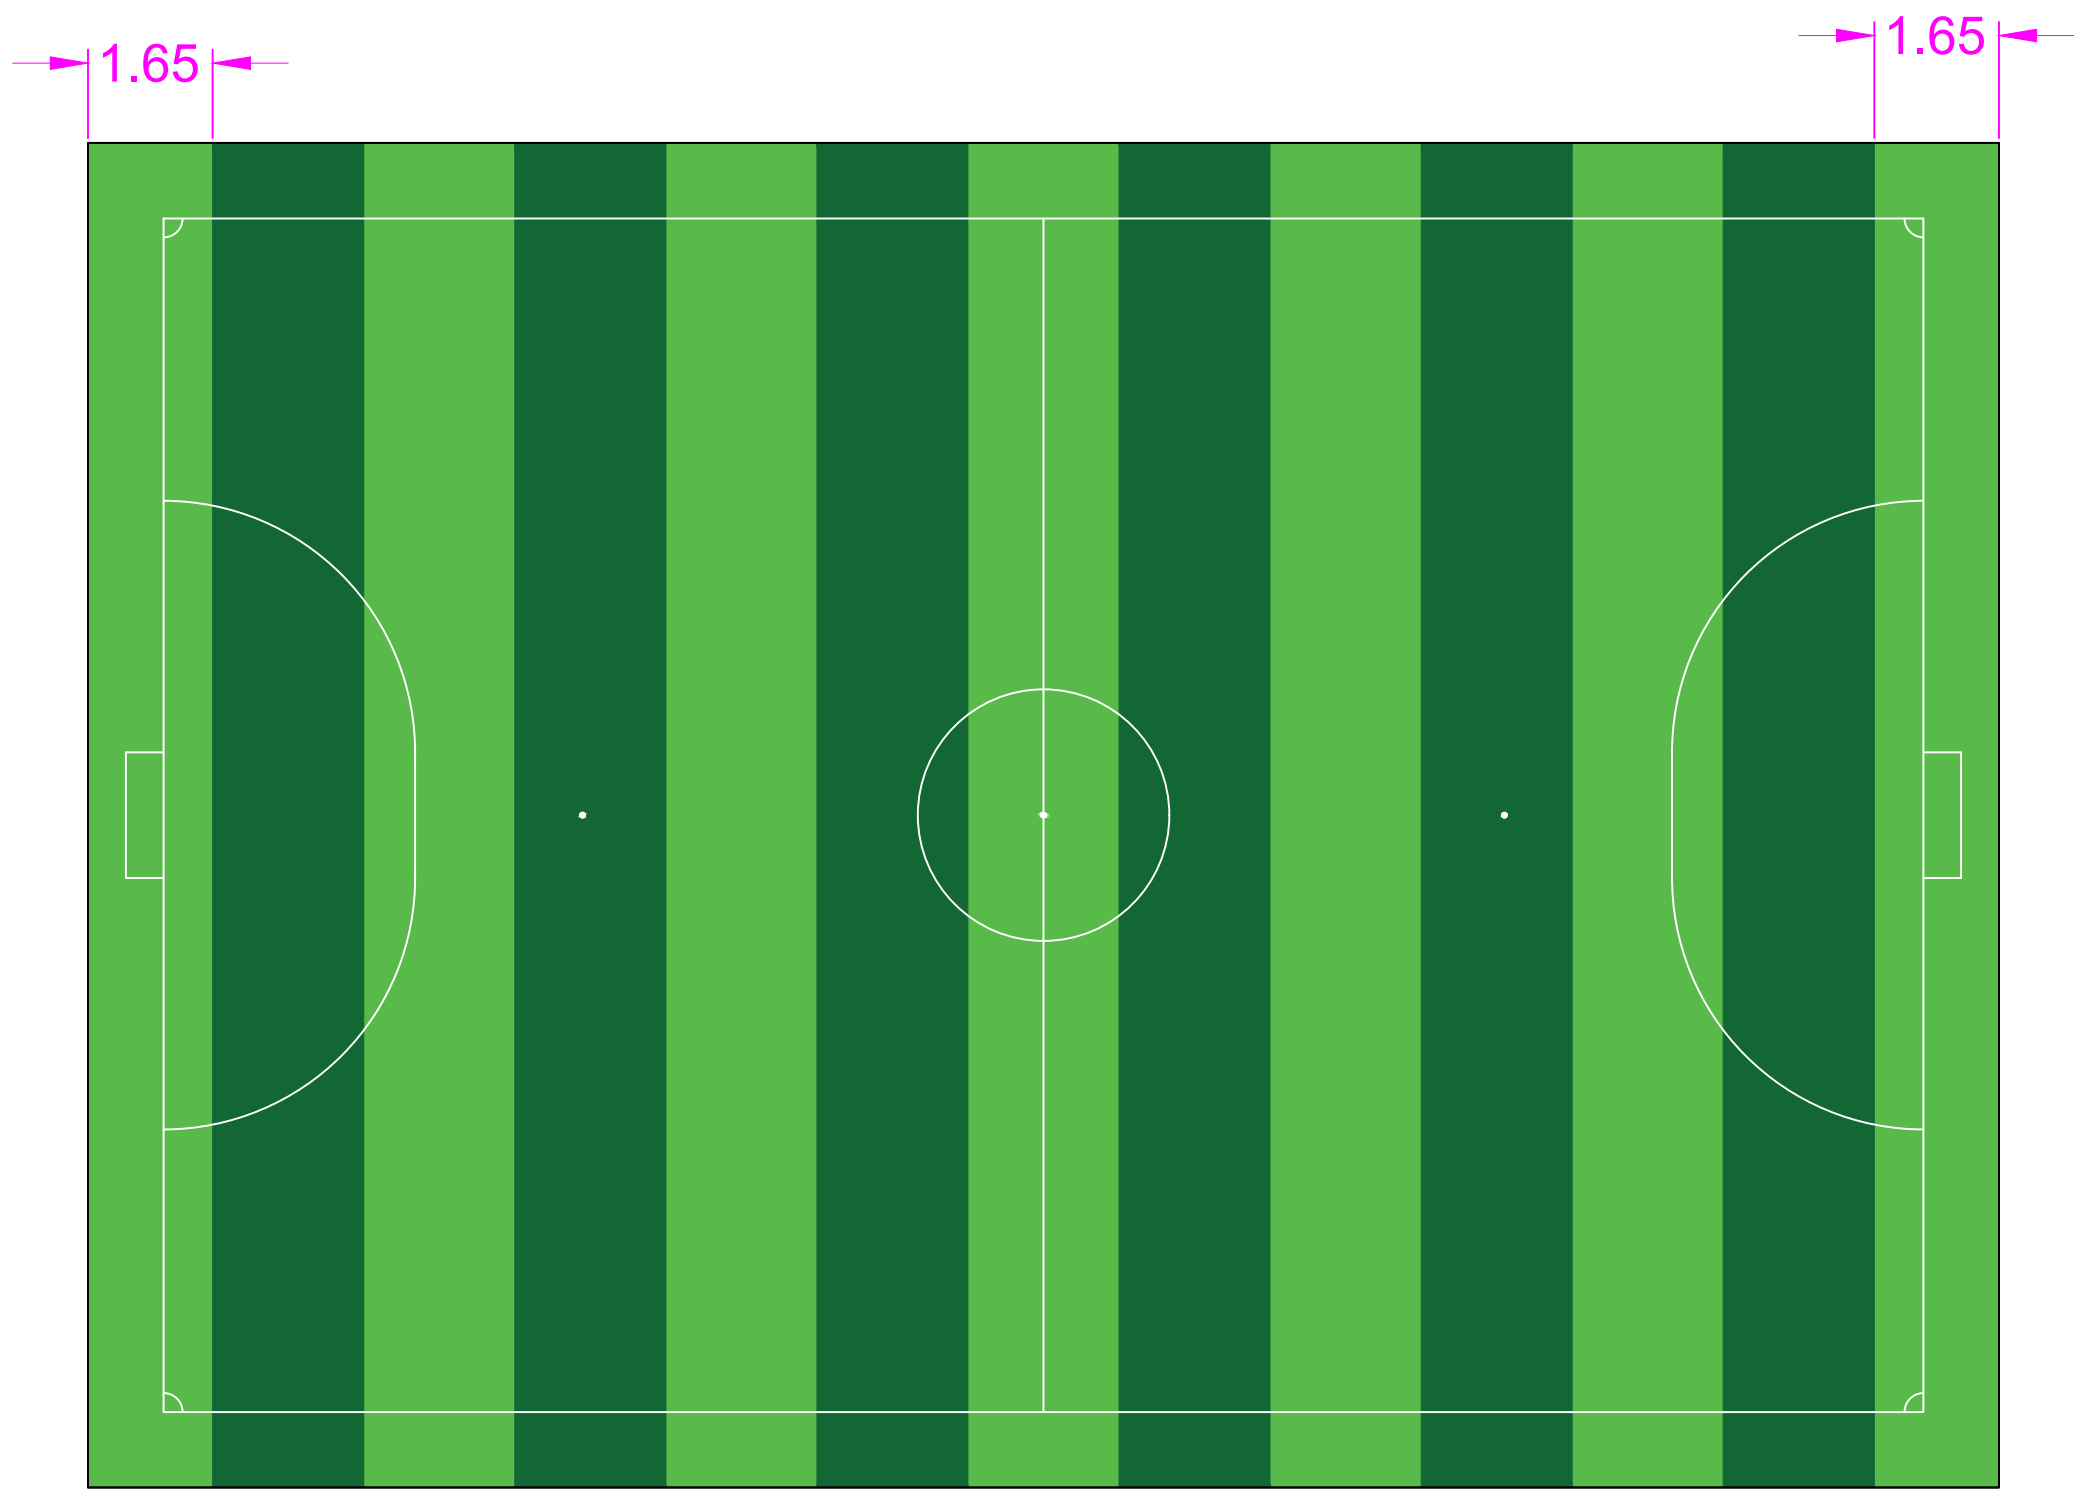


备注：

- 1. 场地比赛区域尺寸23. 3m*15. 80m，白草宽度0. 08m；
- 2. 现场施工时，请按照设计图纸的草卷编号顺序摆放，否则因此造成的铺装问题公司概不承担责任；
- 3. 施工时请按照设计图纸的胶水用量以确保粘接效果。

工程名称	
图纸类型	五人制人造草坪施工图
制图单位	
日期	2026. 7. 30

施工图

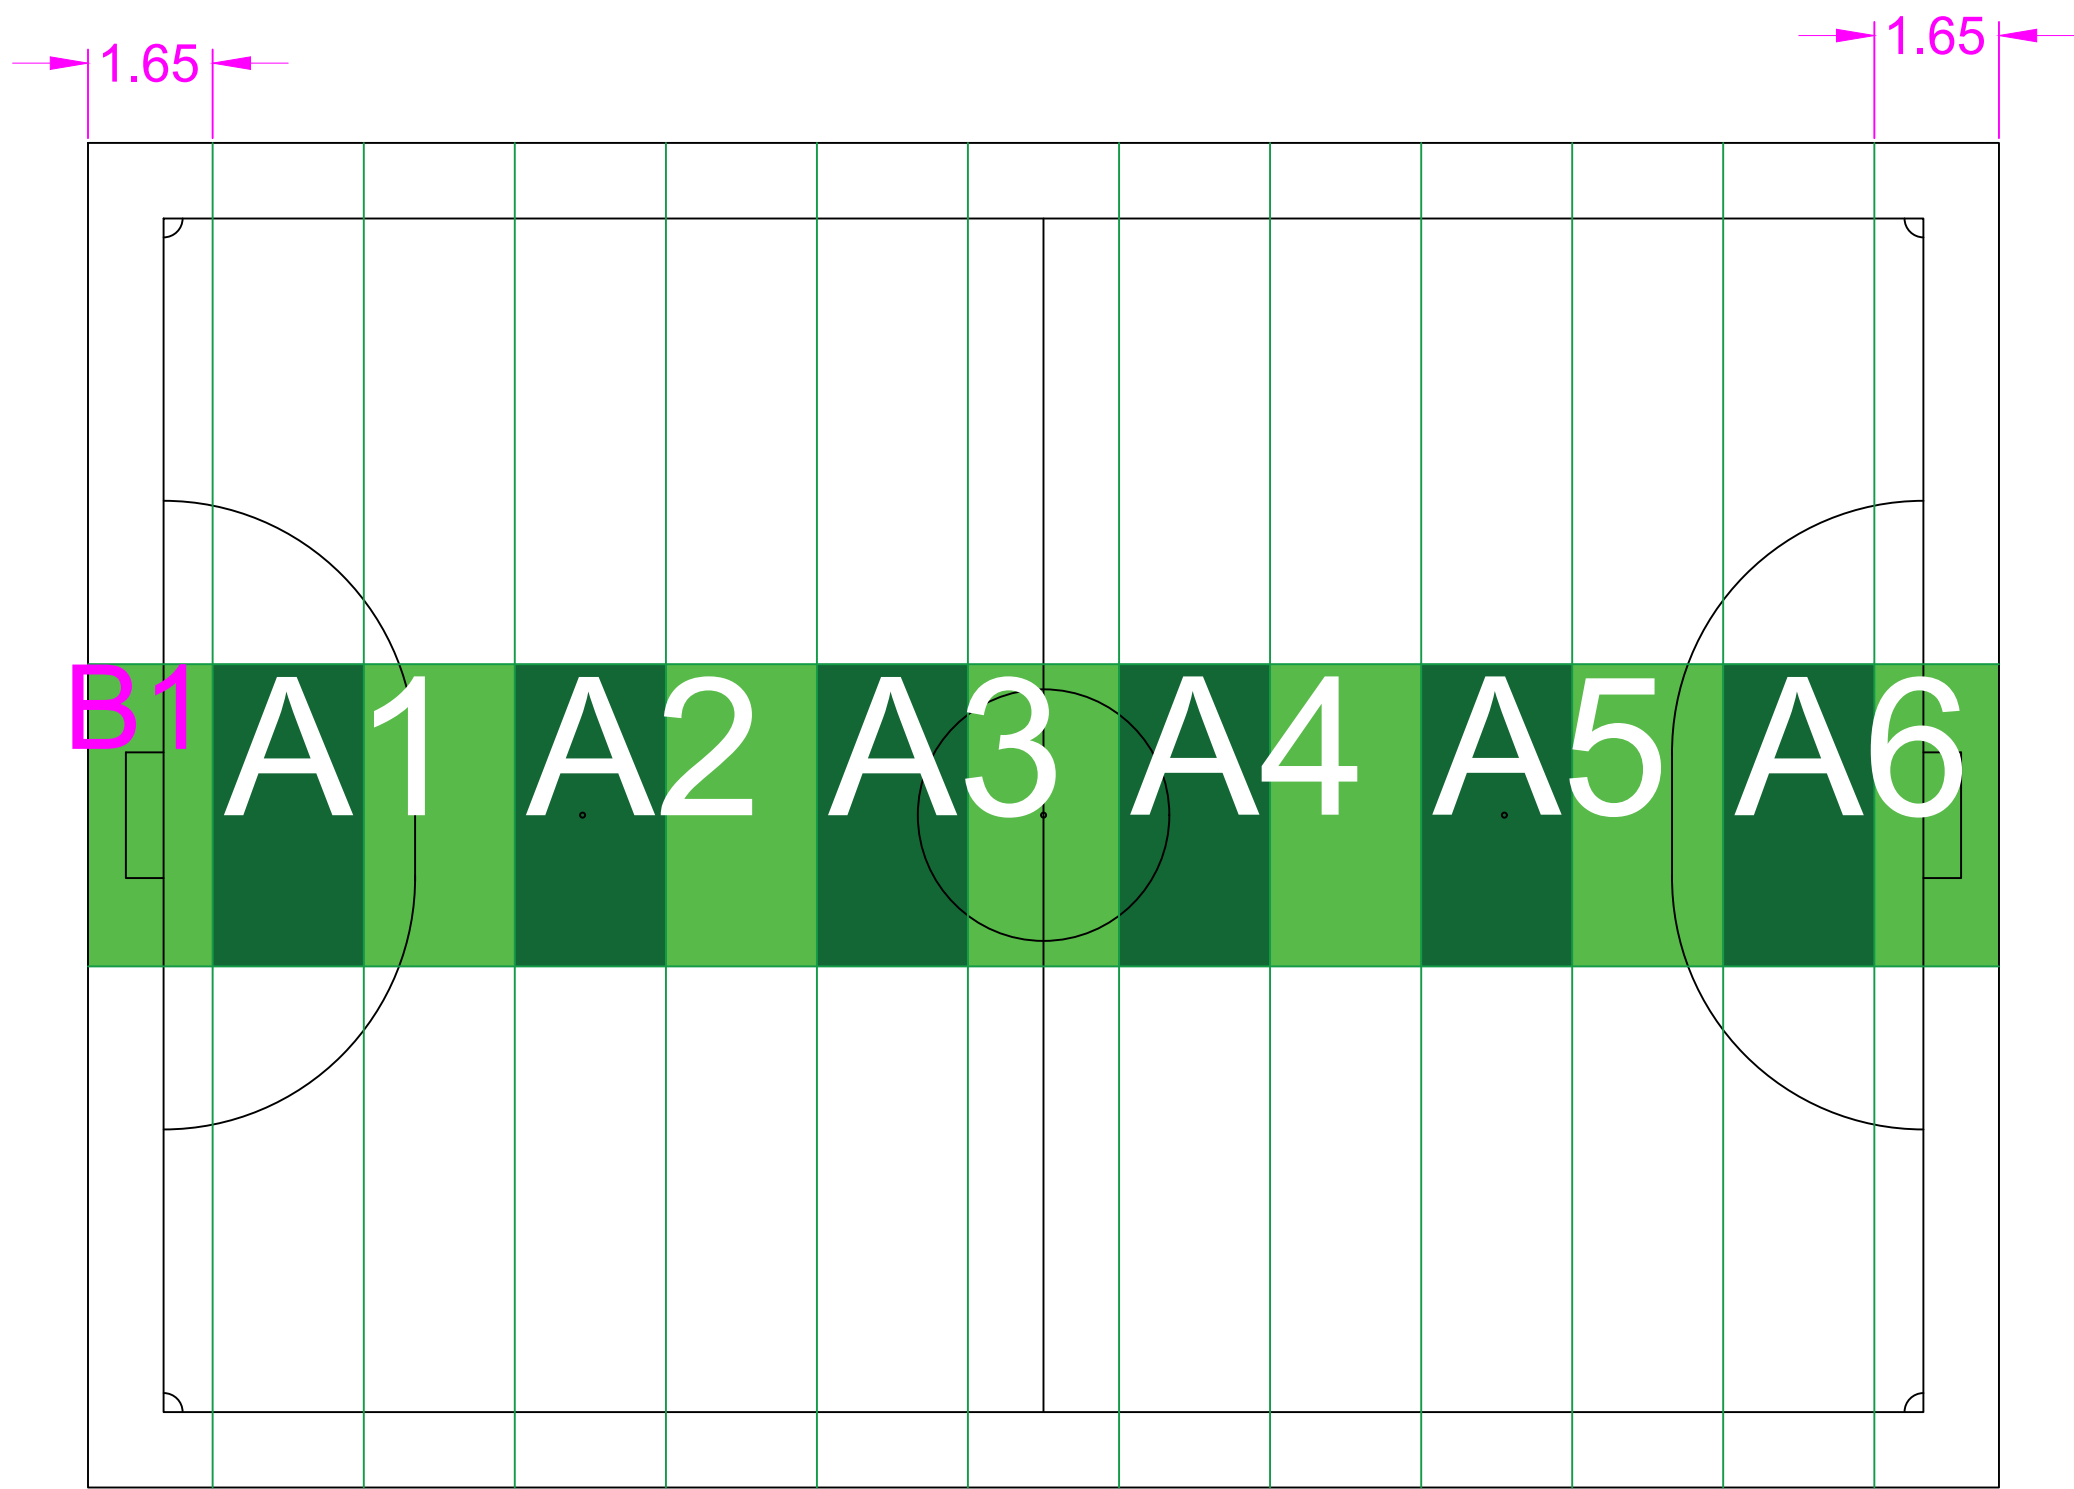

草坪生产方案明细表						
序号	颜色	规格	卷数	单位	数量	编号
1	深浅双色	17. 8*4m	6	m²	427.20	A1-A6
2	浅色	11. 57*2m	1	m²	23.14	B1
3	白草	6*2m	1	m²	13.00	AW1
4	胶水		6	桶		
5	接缝布			米	500	
6	场地实际面积：450. 34m²		实际生产面积：463. 34m²（绿草450. 34m², 白草12m²）			

工程名称	
图纸类型	五人制人造草坪施工图
制图单位	
日期	2026. 7. 30